


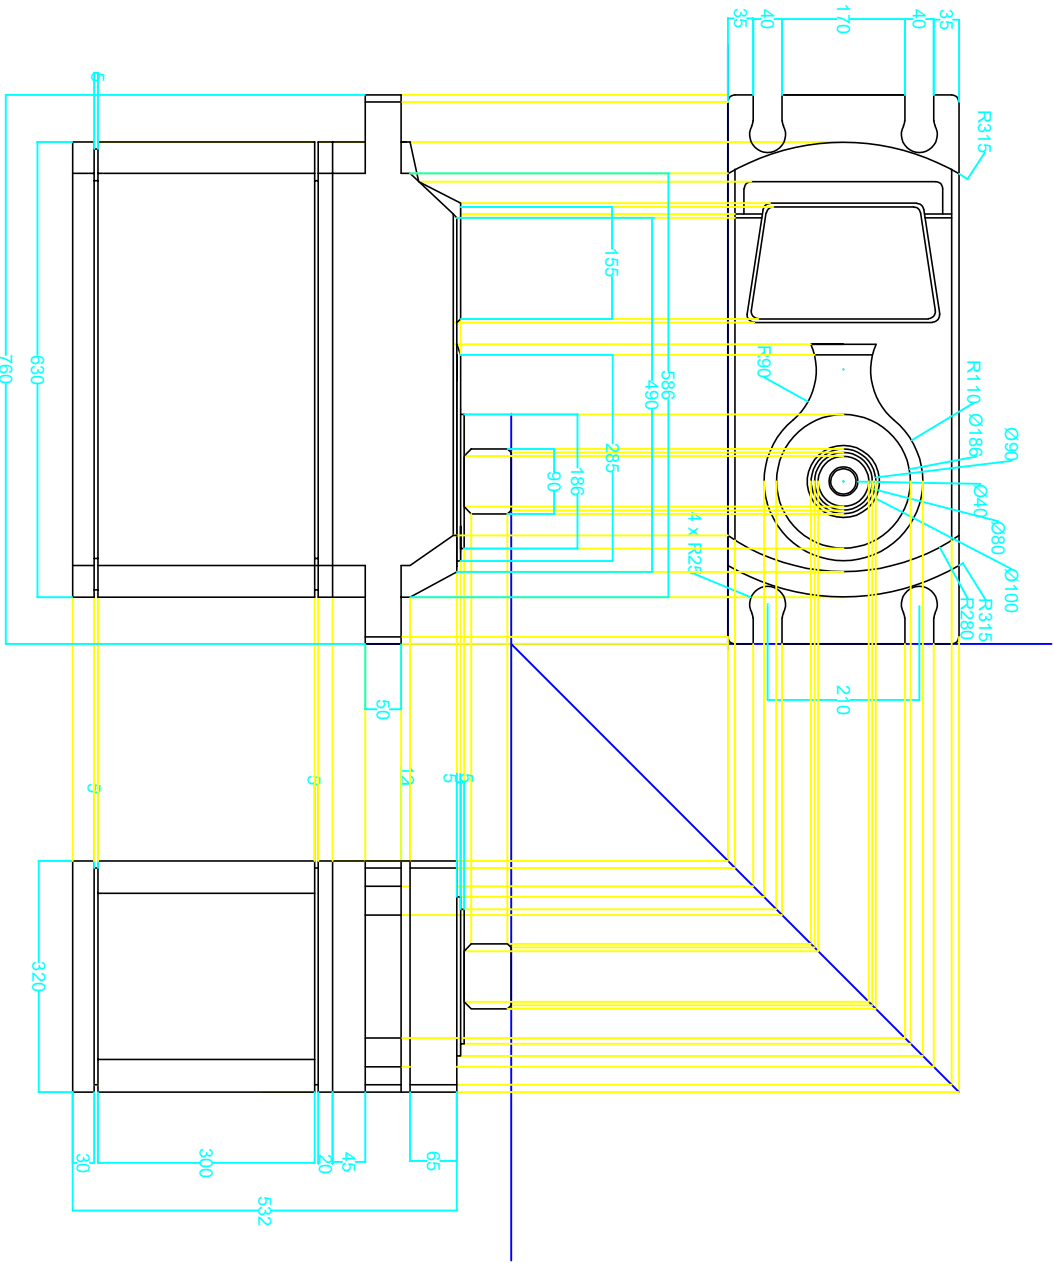

NORTH METROPOLITAN
TAFE

DRAWN: Z CHEN		TITLE: Tile Block	
DATE: Jul. 17, 26			

REVISION 1.1	UNITS: MM	SURFACE ROUGHNESS		
TOLERANCE		SCALE: NTS	MATERIAL: Mild Steel	DRAWING No: 4
				A4